## Draper Office 2nd Floor Workstations

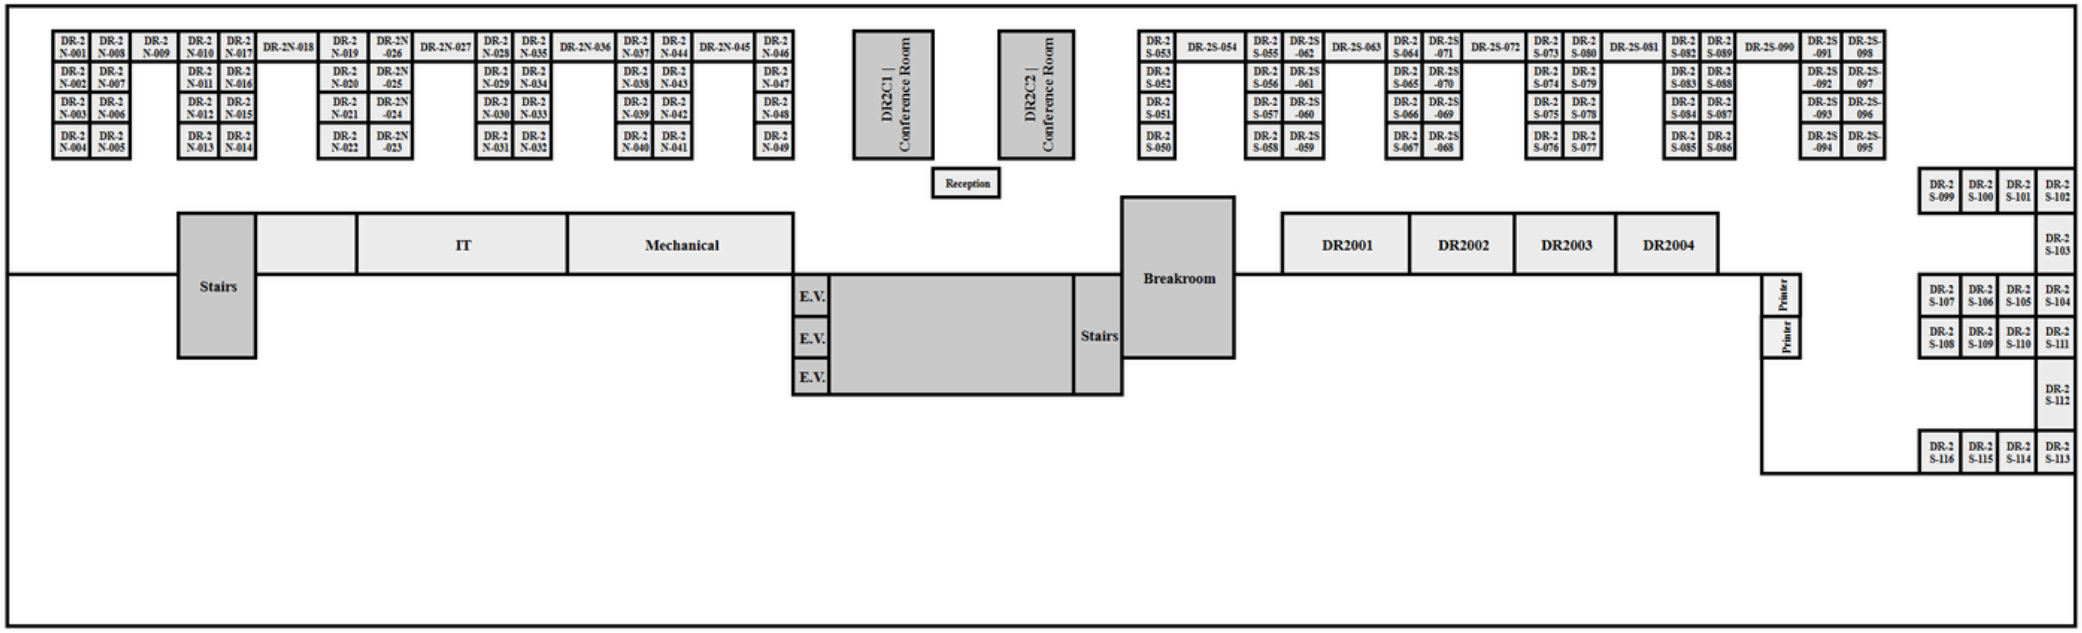

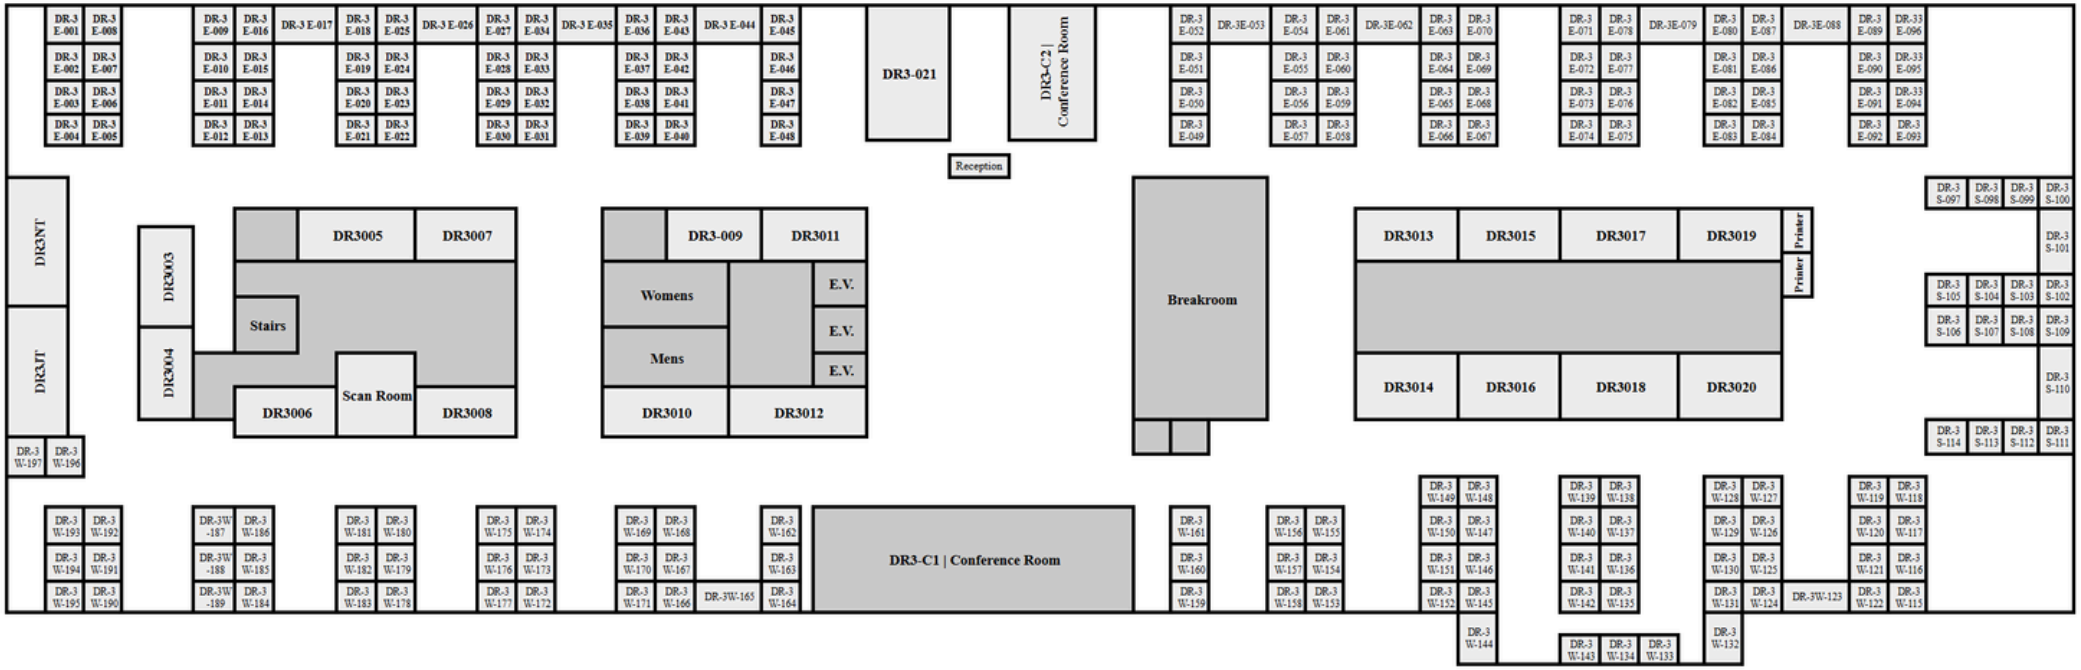
## Draper Office 3rd Floor Workstations